

(CHECKLIST PRIOR TEMPLATE SETTING)

PROJECT NAME: _____

CONTACT NO.: _____

ITEMS	ACTIVITY	CHECKED BY INSTALLER/FOREMAN			DATE	REMARKS	CHECKED BY INSTALLER/FOREMAN			DATE	REMARKS
		Y	N	N/A			Y	N	N/A		
1	Is the gridline set?										
2	Is the centerline set?										
3	Is the drawing has offset? Offset value _____ mm.										
4	Conduct measurement. Are the distances according to plan?										
5	Is the plumbness of shaft acceptable?										
6	Are the separator beam installed?										
7	Total Travel Height as per plan										
8	Pit Depth as per plan										
9	Overhead as per plan										
10	CWT Rail Bracket (min / max)										
11	Main Rail Bracket (min / max)										

REMARKS:

- ☐ Proceed to Installation of Entrance Equipment
- ☐ Proceed to Installation of Rails
- ☐ For punchlist rectification and for reinspection


NAME AND SIGNATURE

DATE

Checked and confirmed by Foreman: _____

Acknowledge by Project Engineer: _____

Verified by QA/QC Inspector: _____

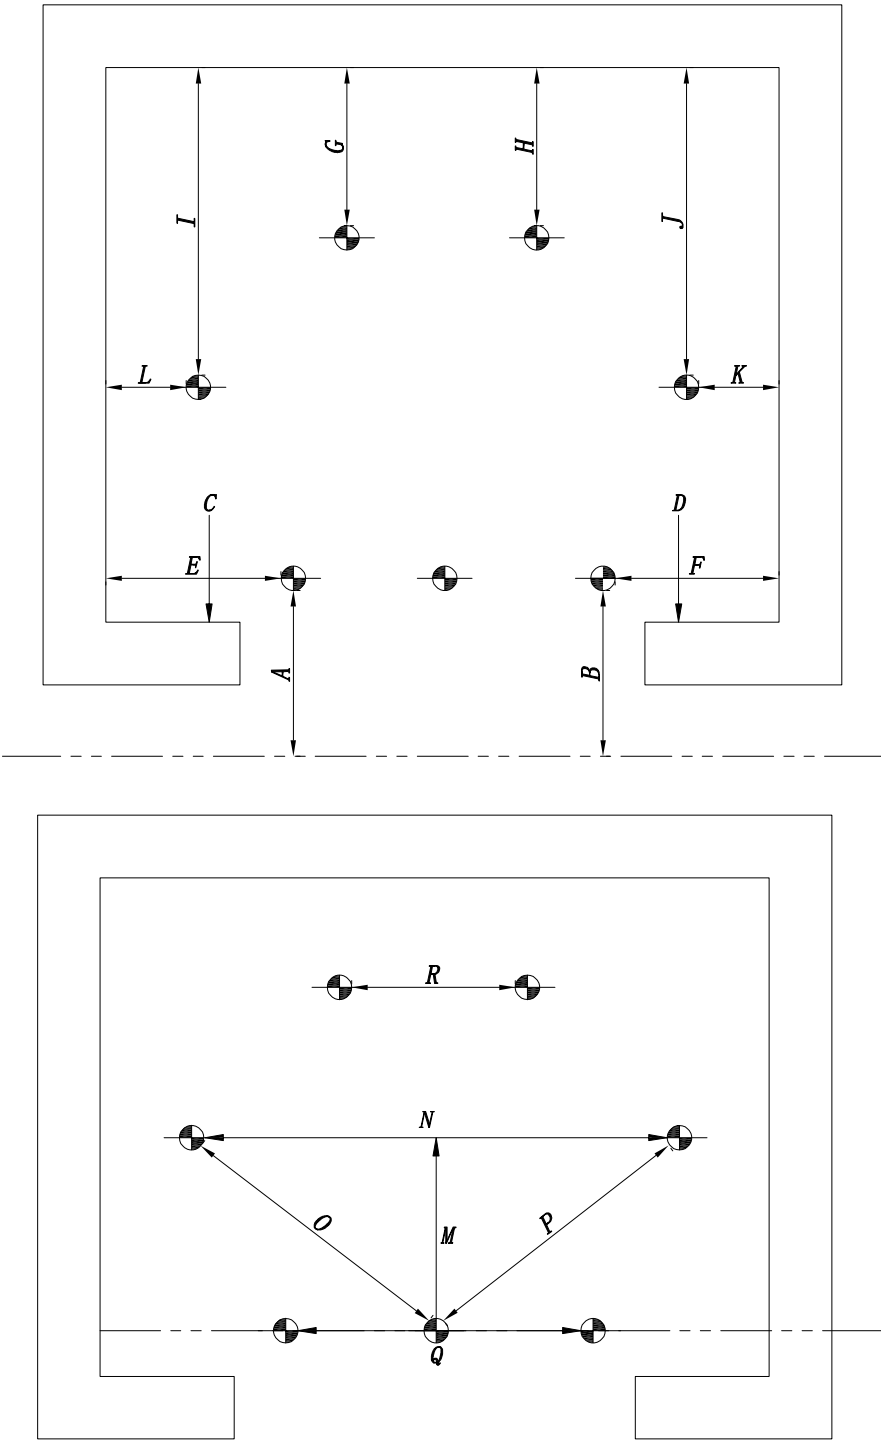


REAR COUNTERWEIGHT

	ALL FLOORS											
FLOOR	A	B	C	D	E	F	G	H	I	J	K	L
REQ'T												
TOP												
3												
4												
5												
6												
7												
BOTTOM												

TEMPLATE AREA (TOP AND BOTTOM)

FLOOR	M	N	O	P	Q	R
REQ'T						
TOP						

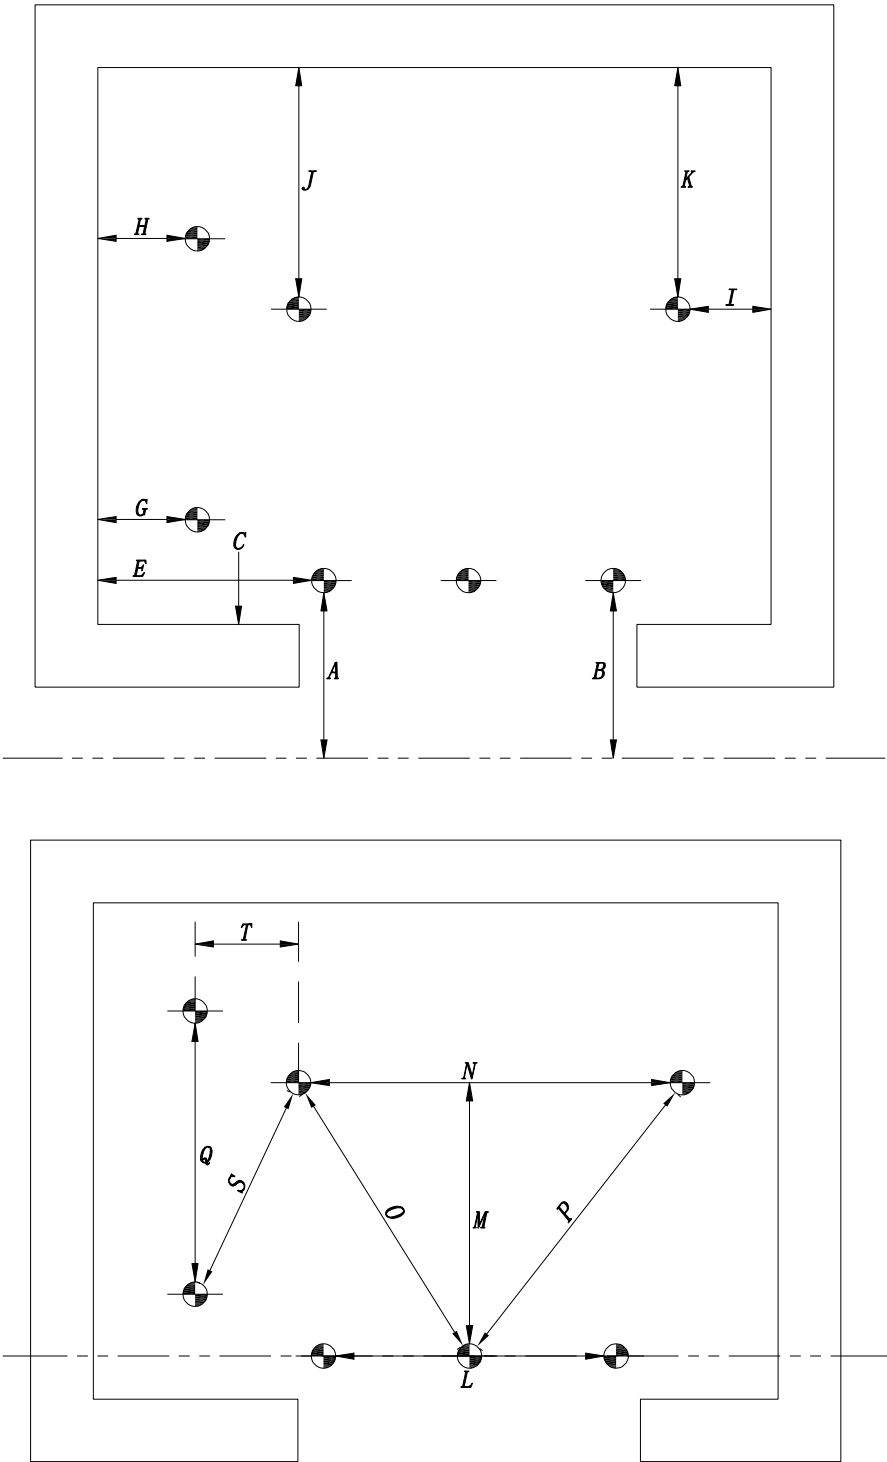


LEFT COUNTERWEIGHT

	ALL FLOORS										
FLOOR	A	B	C	D	E	F	G	H	I	J	K
REQ'T											
TOP											
3											
4											
5											
6											
7											
BOTTOM											

TEMPLATE AREA (TOP AND BOTTOM)

FLOOR	L	M	N	O	P	Q	R	S	T
REQ'T									
TOP									

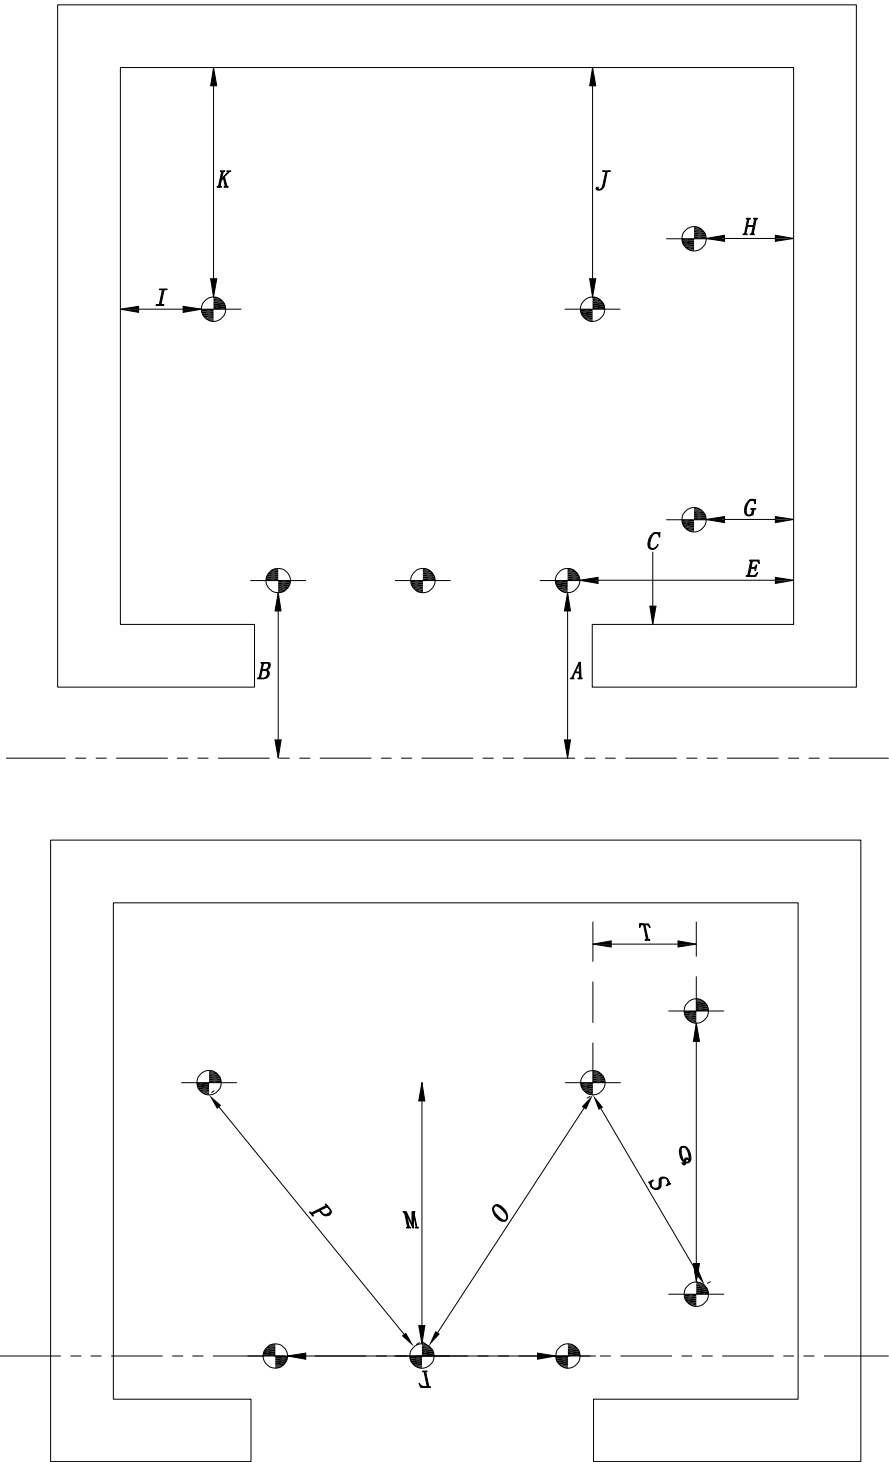


RIGHT COUNTERWEIGHT

	ALL FLOORS										
FLOOR	A	B	C	D	E	F	G	H	I	J	K
REQ'T											
TOP											
3											
4											
5											
6											
7											
BOTTOM											

TEMPLATE AREA (TOP AND BOTTOM)

FLOOR	L	M	N	O	P	Q	R	S	T
REQ'T									
TOP									

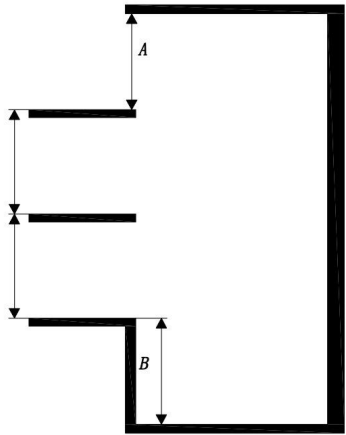

	REQUIRED	FOREMAN/INSTALLER	QA/QC INSPECTOR	REMARKS
OVERHEAD (A)				
PIT DEPTH (B)				
FLOOR TO FLOOR HEIGHT				